


16

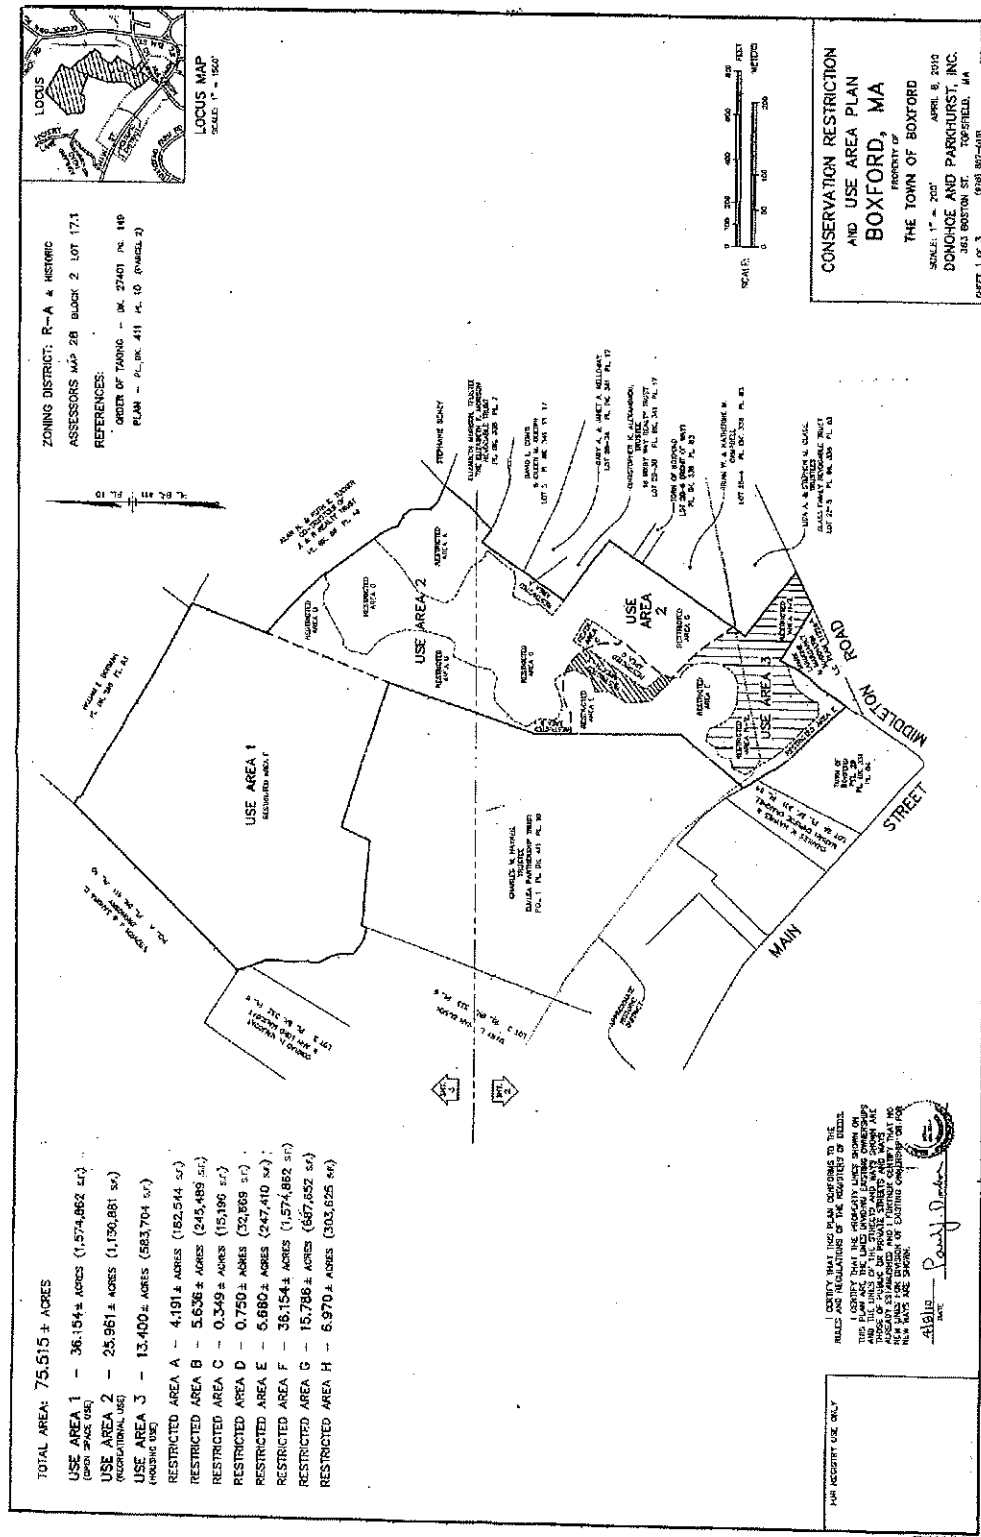

17

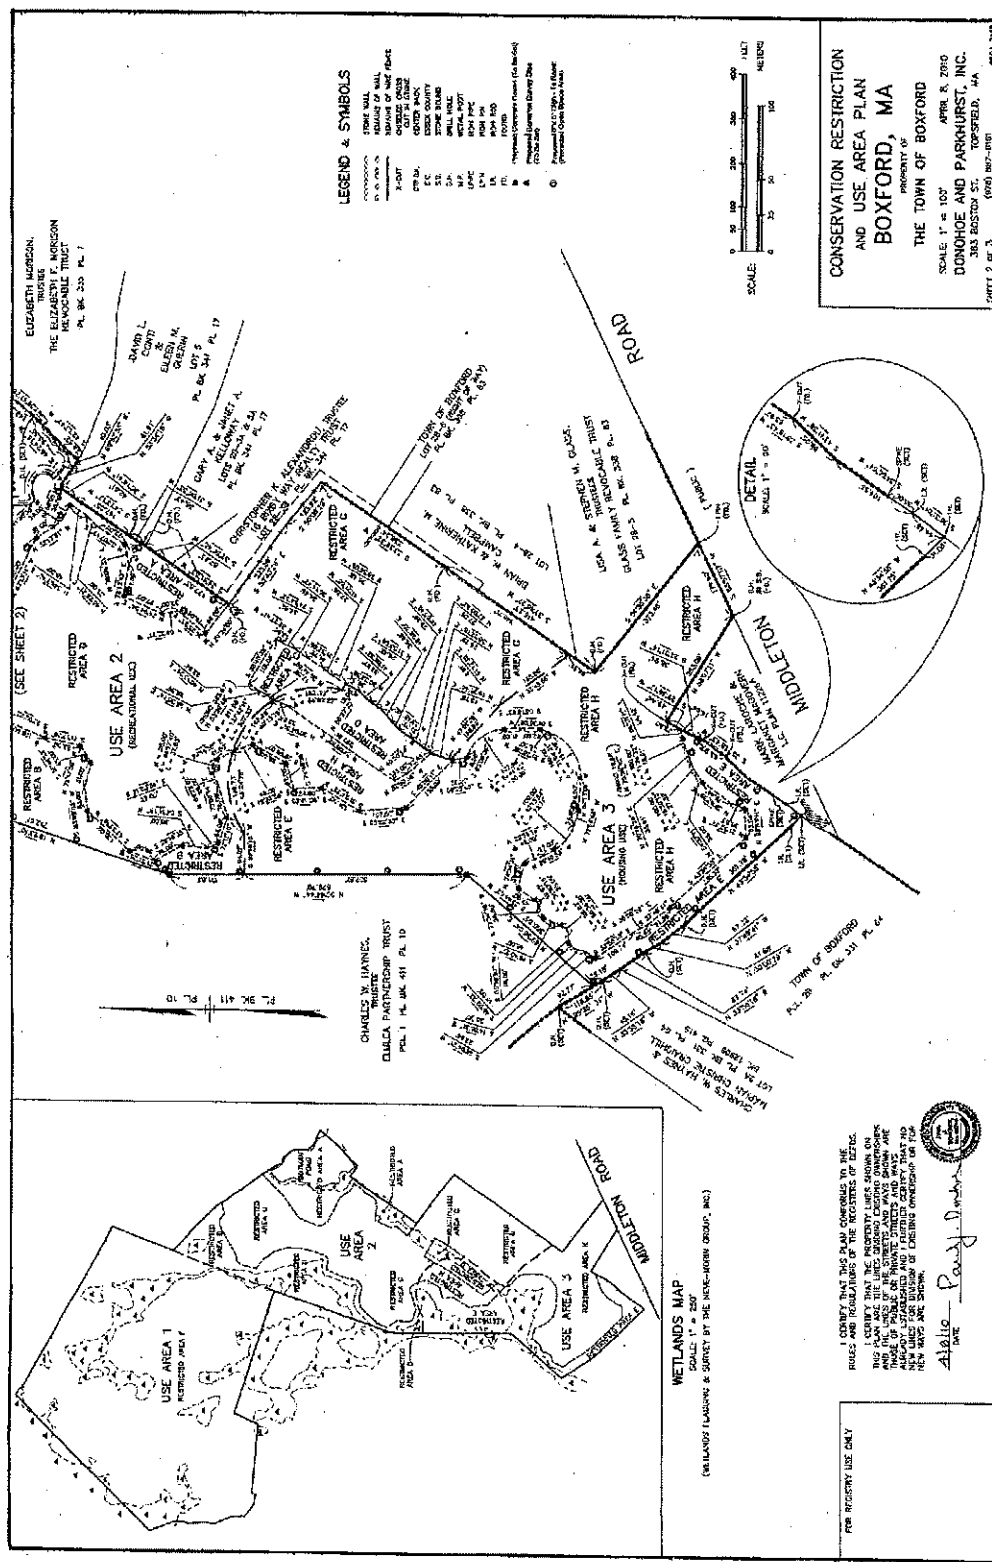


Exhibit A – Reduced Copy of Plan of the Premises (Sheet 3)

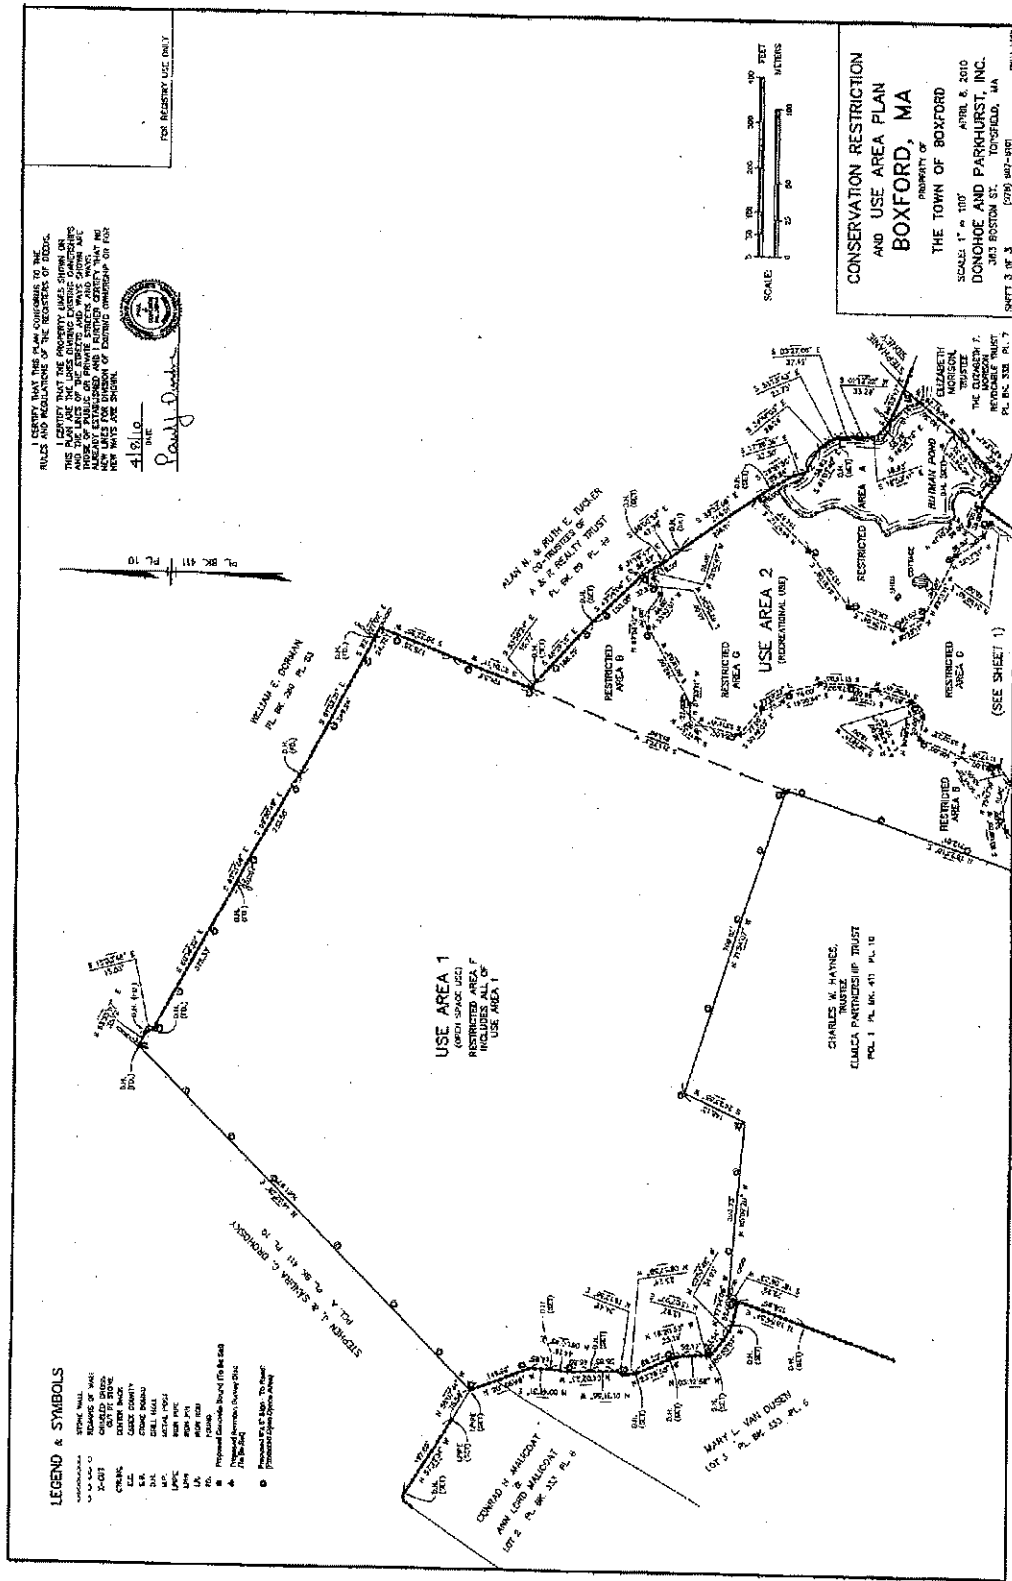


Exhibit B – Copy of Order of Taking (Page 1)

8
13

COMMONWEALTH OF MASSACHUSETTS

20071219000133 Bk:27401 Pg:149
12/19/2007 10:48:00 OTHER Pg 1/6

Essex County, ss.

TOWN OF DOXFORD

ORDER OF TAKING

At a regularly convened meeting of the Board of Selectmen of the Town of
Boxford (hereinafter "TOWN") held this 17th day of December, 2007 it was voted and
ordered:

The Board of Selectmen of the Town, duly elected, qualified, and acting as such,
on behalf of the Town and by virtue of and in accordance with the authority of the
provisions of Chapter 40, Section 14 and Chapter 79 of the General Laws, as amended,
and of any and every other power and authority which is hereunto in any way enabling,
does hereby take for the purposes set forth in the Community Preservation Act (Chapter
44B) of the fee in the land the land located on Middleton Road and shown as Parcel 2 on
plan entitled "Plan of Land in Boxford, MA Property of Charles W. Haynes, Trustee
Elmlea Partnership Trust" Scale: 1" = 100' dated November 12, 2007 made by Donohoe
and Parkhurst, Inc. and recorded with Essex South District Registry of Deeds in Plan
Book 411, Plan 10, containing 75.515 acres, more or less.

Any and all trees and structures upon the land are specifically included in this
taking.

Said land is owned or supposed to be owned by Charles W. Haynes, Trustee of
the Elmlea Partnership Trust under Declaration of Trust dated October 30, 1996 and
recorded with Essex South District Registry of Deeds in Book 13826, Page 481.

If the name of the Owner is not correctly stated, the name of the supposed Owner
being given as of this Order of Taking, it is understood that in such instance the land
referred to is owned by an owner or owners unknown to us.

For damages sustained by the following Owner and his property by reason of the
foregoing taking, and in accordance with the provisions of M.G.L. Chapter 79, Section 6,
as amended, the following award is made. The Town reserves the right to amend the
award at any time prior to the payment thereof for good cause shown. The award hereby
made is set forth in annex "A" which annex "A" is not to be recorded in the Registry of
Deeds with this Order of Taking.

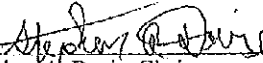
<u>Address/Description</u>	<u>Supposed Owners</u>	<u>Area</u>
Parcel 2, Middleton Road	Charles W. Haynes, Trustee of Elmlea Partnership Trust	75.515 acres

Exhibit B – Copy of Order of Taking (Page 2)


No betterments are to be assessed under this Taking.


IN WITNESS WHEREOF, we, the duly elected and qualified Selectmen of the Town of Boxford have hereunto set our hands this 17th day of December, 2007


BOARD OF SELECTMEN
TOWN OF BOXFORD


Stephen A. Davis, Chair


Charles J. Costello

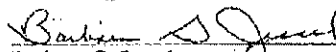
Barbara G. Jessel

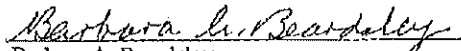

Barbara A. Beardsley

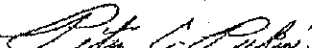
Peter C. Perkins

COMMONWEALTH OF MASSACHUSETTS

Essex ss.

On this 18th day of December, 2007, before me, the undersigned Notary Public, personally appeared Board of Selectmen, who proved to me through satisfactory evidence of identification, which were personal knowledge, to be the person whose name is signed on the preceding or attached document, and acknowledged to me that he/she signed it voluntarily for its stated purpose, as Selectman on behalf of the Inhabitants of the Town of Boxford.

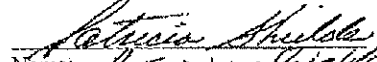
Name: Patricia A. Shields
Notary Public
My commission expires:



PATRICIA A. SHIELDS
Notary Public
Commonwealth of Massachusetts
My Commission Expires
September 27, 2013