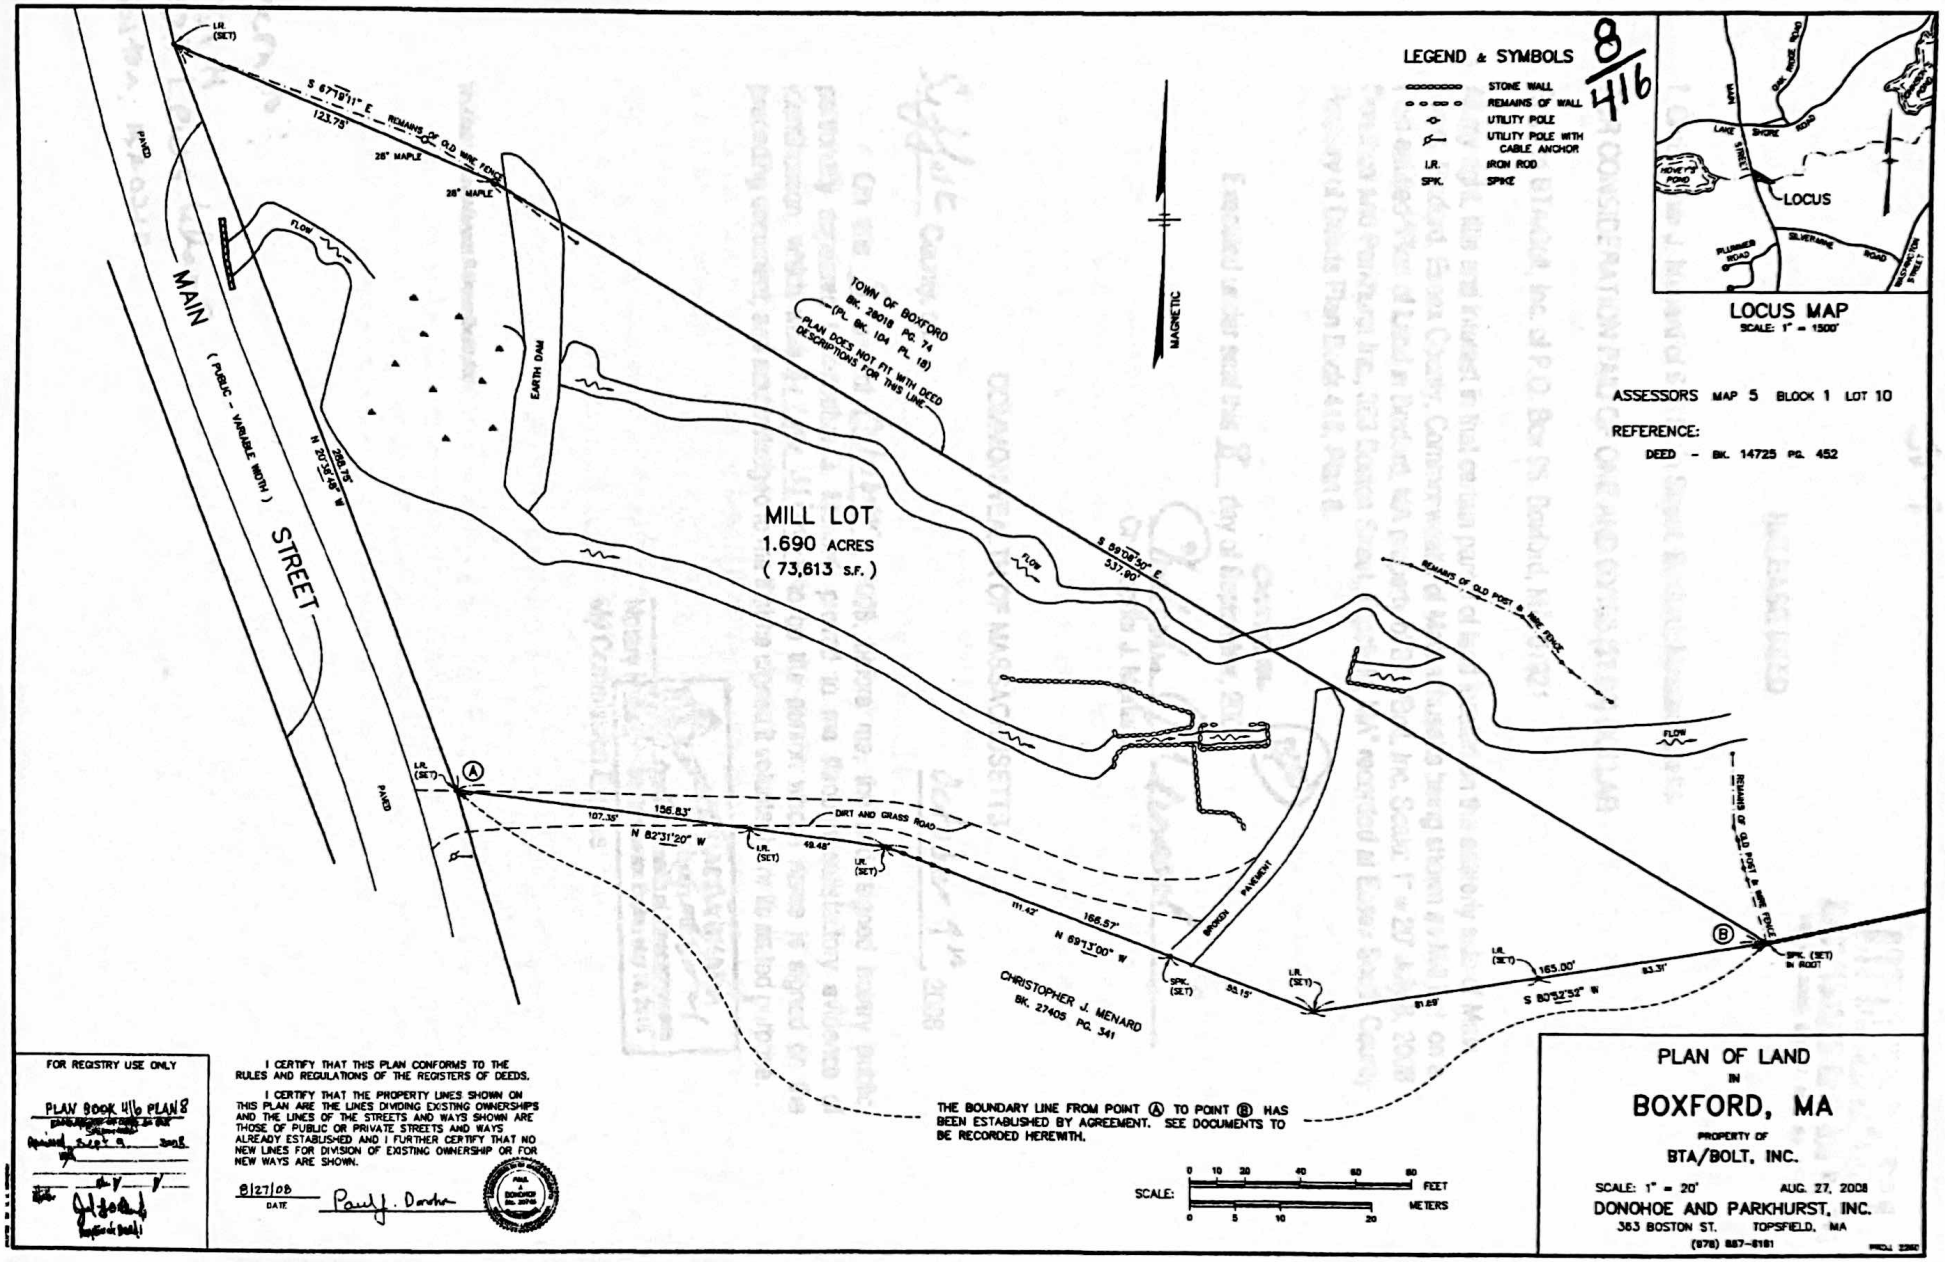

8/416
LEGEND & SYMBOLS
STONE WALL
REMAINS OF WALL
UTILITY POLE
UTILITY POLE WITH CABLE ANCHOR
I.R. IRON ROD
SPK. SPIKE
LOCUS MAP
SCALE: 1" = 1500'
LOCUS
MAIN STREET
LAKE SHORE ROAD
MOVE'M POND
PLUMMER ROAD
SILVERMINE ROAD
ASSESSORS MAP 5 BLOCK 1 LOT 10
REFERENCE:
DEED - BK. 14725 PG. 452
MAIN STREET (PUBLIC - VARIABLE WIDTH)
PAVED
LR. (SET)
S 67°18'11" E 123.75'
REMAINS OF OLD WIRE FENCE
28" MAPLE
FLOW
EARTH DAM
TOWN OF BOXFORD BK. 26018 PG. 74 (PL. BK. 104 PL. 18)
PLAN DOES NOT FIT WITH DEED DESCRIPTIONS FOR THIS LINE
MAGNETIC
MILL LOT
1.690 ACRES
(73,613 S.F.)
N 20°35'48" W 208.75'
S 88°04'50" E 537.90'
REMAINS OF OLD POST & WIRE FENCE
DIRT AND GRASS ROAD
N 82°31'20" W 107.39' 156.83'
48.48'
111.43' 166.57'
N 89°13'00" W
BROKEN PAVEMENT
83.15'
81.89'
165.00'
83.31'
S 80°52'52" W
SPK. (SET) IN ROOT
CHRISTOPHER J. MENARD BK. 27405 PG. 341
THE BOUNDARY LINE FROM POINT A TO POINT B HAS BEEN ESTABLISHED BY AGREEMENT. SEE DOCUMENTS TO BE RECORDED HEREWITH.
SCALE: 0 10 20 40 60 80 FEET
0 5 10 20 METERS
FOR REGISTRY USE ONLY
PLAN BOOK 416 PLAN 8
I CERTIFY THAT THIS PLAN CONFORMS TO THE RULES AND REGULATIONS OF THE REGISTERS OF DEEDS.
I CERTIFY THAT THE PROPERTY LINES SHOWN ON THIS PLAN ARE THE LINES DIVIDING EXISTING OWNERSHIPS AND THE LINES OF THE STREETS AND WAYS SHOWN ARE THOSE OF PUBLIC OR PRIVATE STREETS AND WAYS ALREADY ESTABLISHED AND I FURTHER CERTIFY THAT NO NEW LINES FOR DIVISION OF EXISTING OWNERSHIP OR FOR NEW WAYS ARE SHOWN.
8/27/08
DATE
Paul J. Donahue
PLAN OF LAND
IN
BOXFORD, MA
PROPERTY OF
BTA/BOLT, INC.
SCALE: 1" = 20' AUG. 27, 2008
DONOHOE AND PARKHURST, INC.
363 BOSTON ST. TOPSFIELD, MA
(978) 887-8181