

8

MERID

PEAKE

27-1-11

BROOK

Connection To Ericson Woods


BERRY

7

SHEETS 3 & 6
(SEE INDEX)

6


pg 1
Berry Patch sub ÷
Washburn
2/2/88

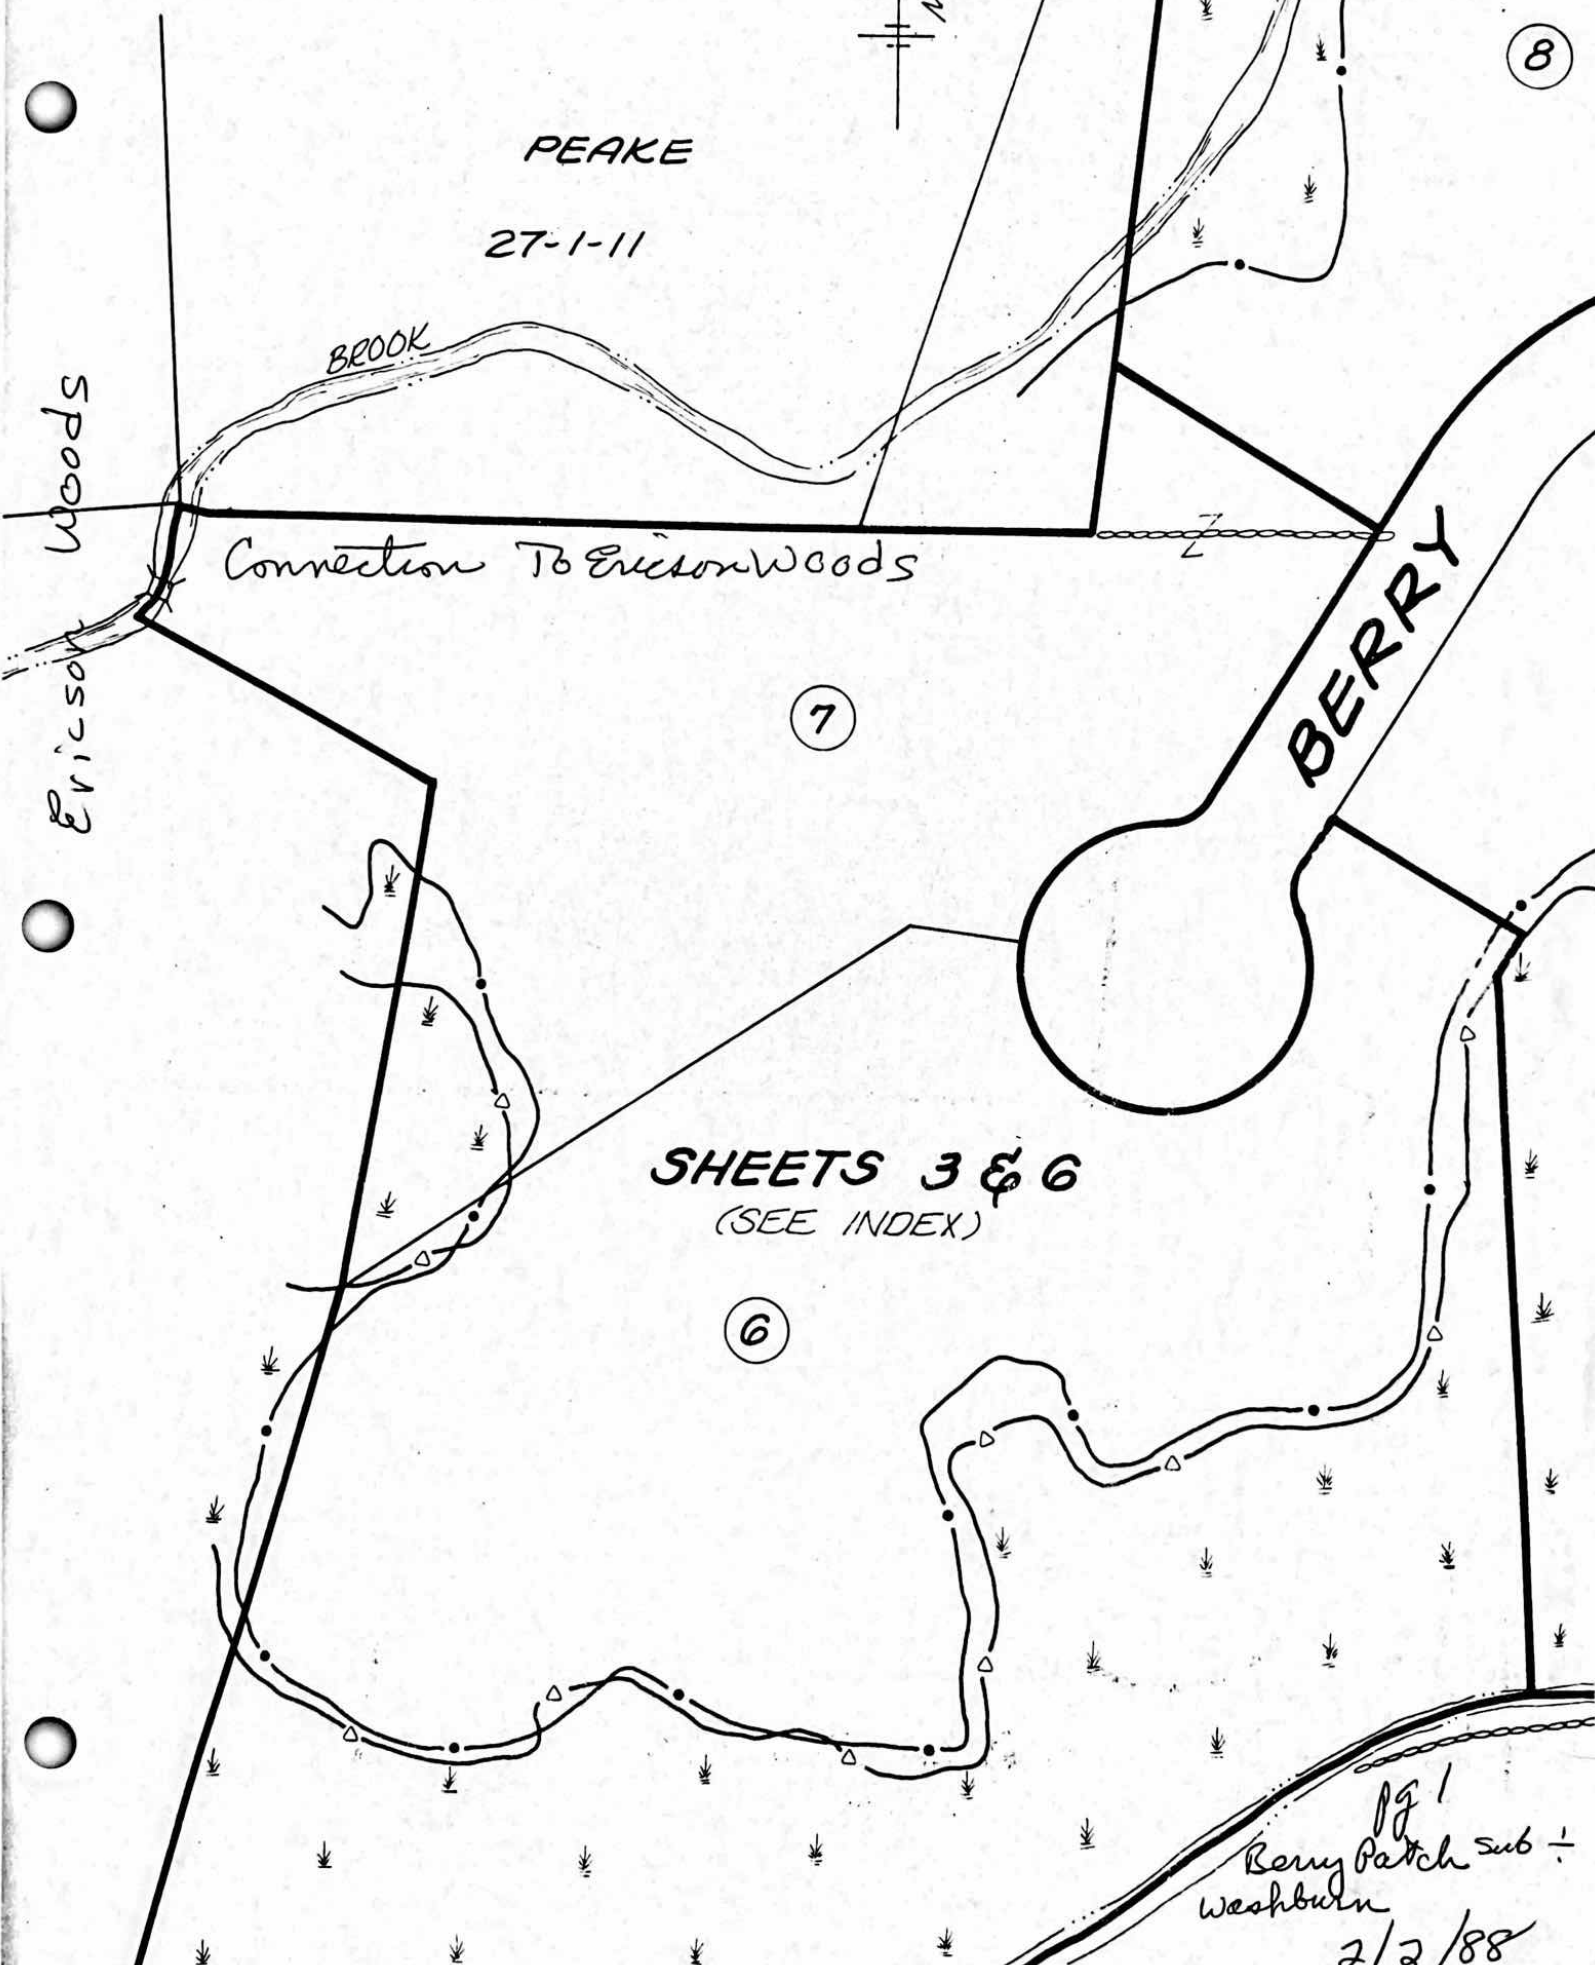

SANDRA M. PEAK

ROBERT & ELIZABETH
HACKING

Elison Woods

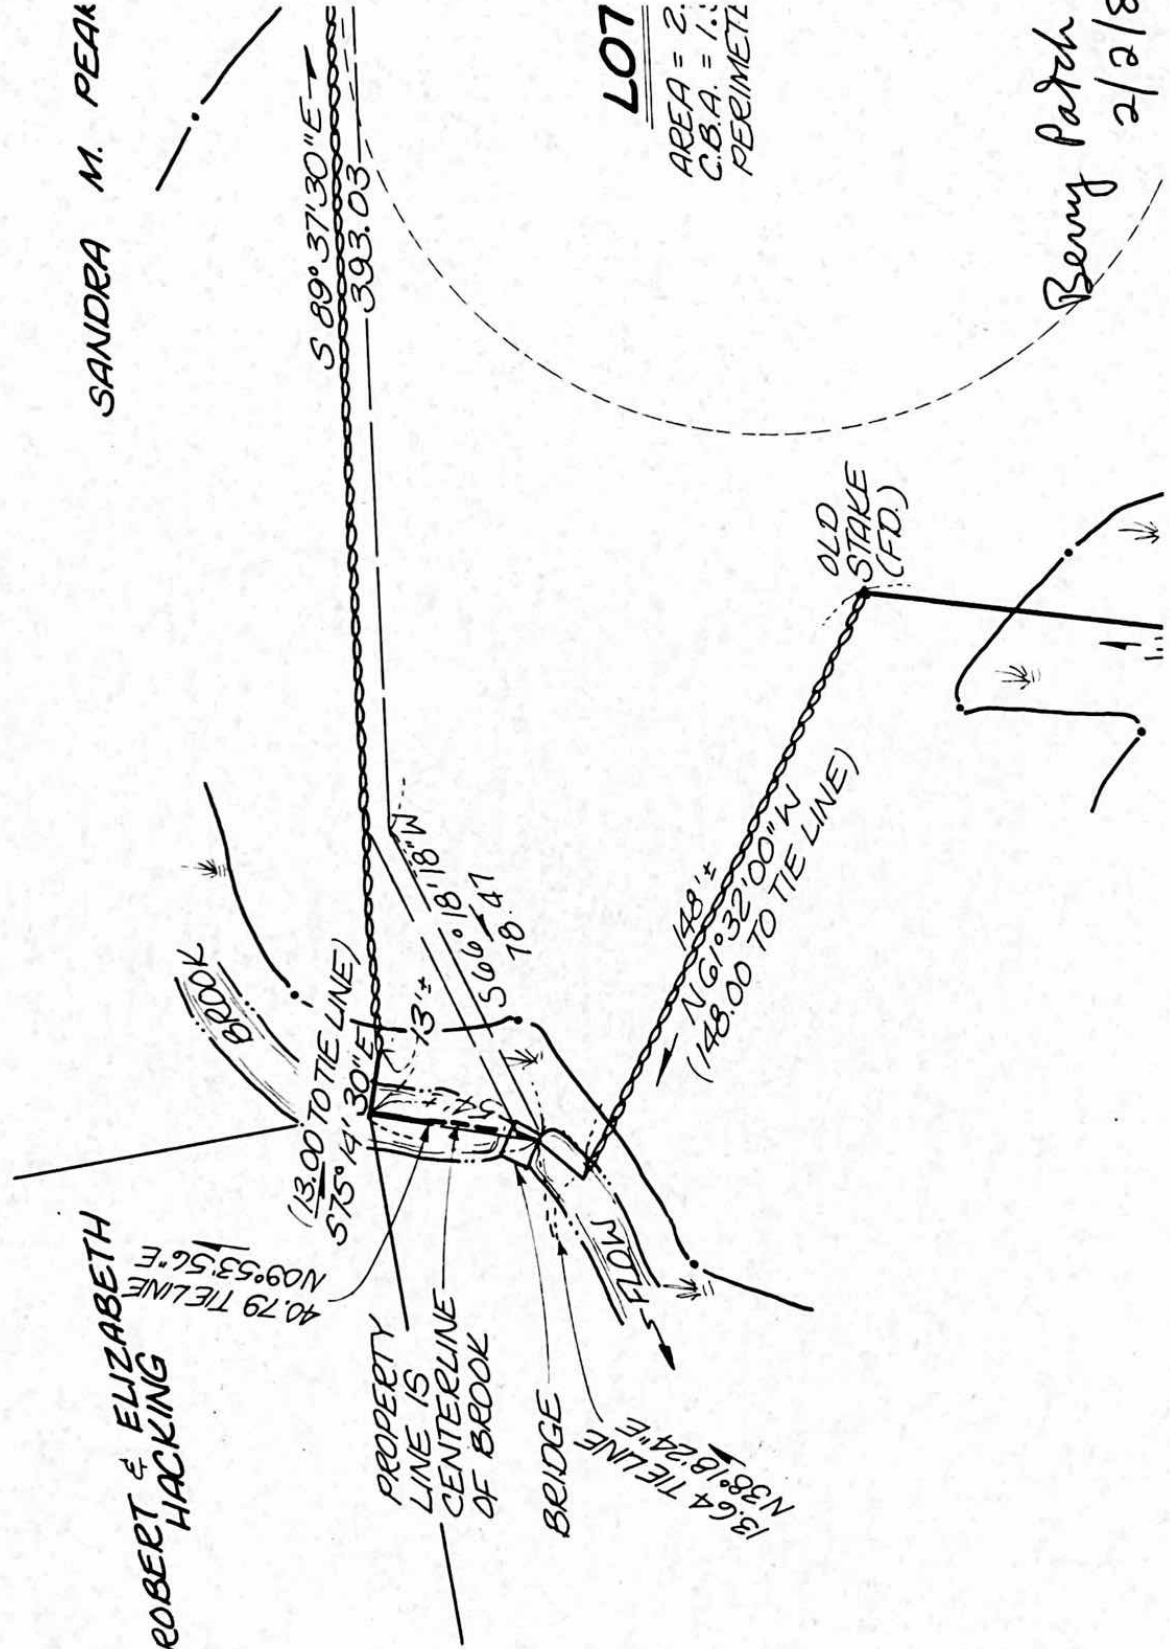


LOT

AREA = 2.
C.B.A. = 1.
PERIMETER

Berry Patch Sub. ÷
2/2/88

HACKING
Ericson Woods

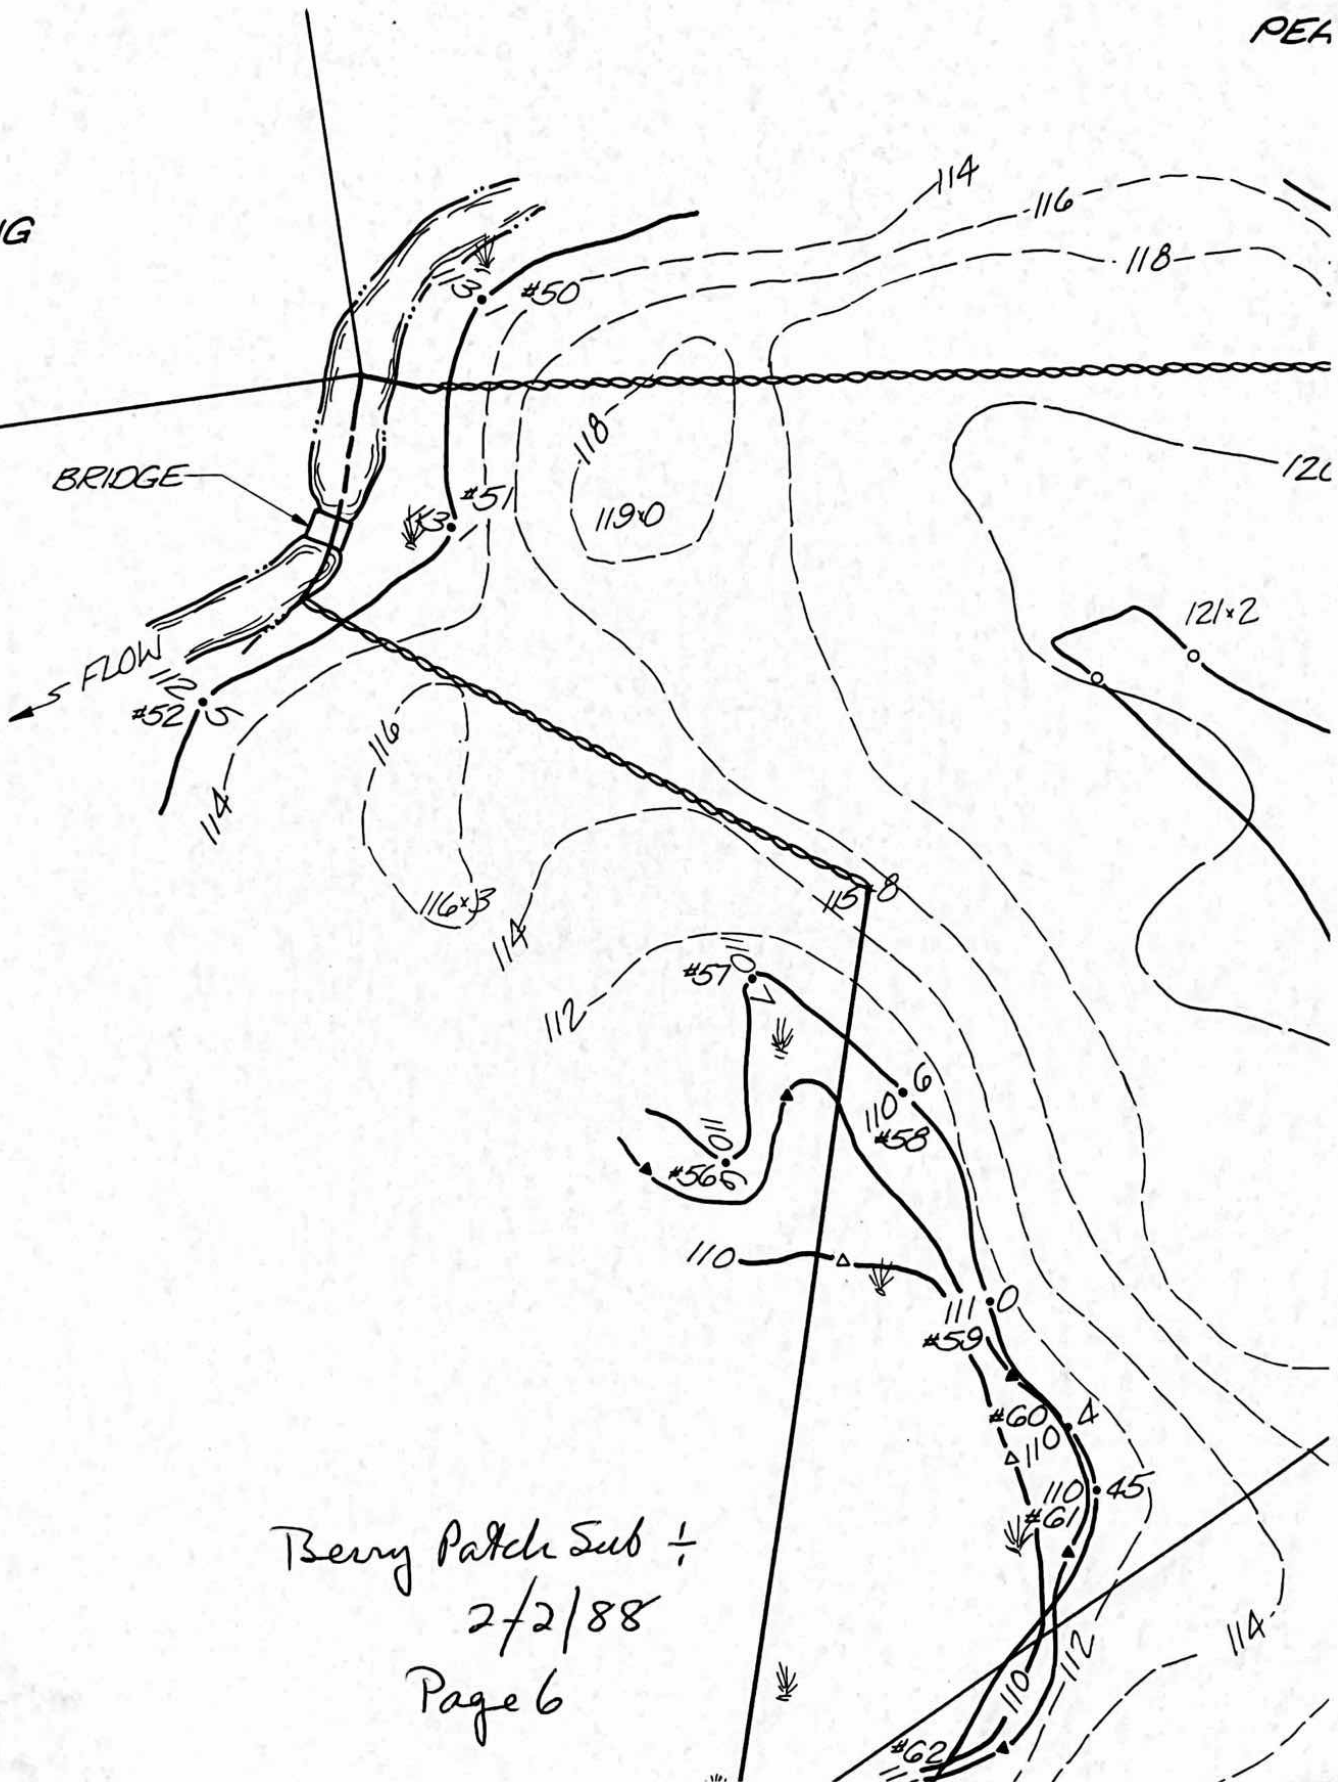

Berry Patch Sub 1/2
2/2/88
Page 6

BOX-O Ericson/BTA/BOLT Conservation Restriction



Greenbelt CRs



Greenbelt Fee Properties



0 50 100 200 Feet

Color orthophotos provided by MassGIS.
1:5,000. Photos taken April 2001.

Boundaries are approximate, and based
primarily on assessor's data.

Map produced by Essex County Greenbelt.
March 2007




BOX-O Ericson/BTA/BOLT Conservation Restriction



Legend

-  Greenbelt Fee Properties
-  Greenbelt CRs

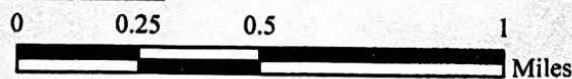

USGS quadrangles provided by MassGIS.
1:25,000.

Boundaries are approximate, and based
primarily on assessor's data.

Map produced by Essex County Greenbelt.
March 2007



35
144

N/F Winthrop P. Haynes et al.

N/F John F. Noyes

Robert M. & Elizabeth L. Hacking
Remaining land A=15² Acres
(See plan in Pl. Bk 147, Pl. 16)

N/F Edward K. Mortimer

N/F Helen K. Atwood

A=10.1041² ACRES

N/F Rosamond L. Lord

Estate of Archie Peabody

PLAN OF LAND IN BOXFORD

Property of
ROBERT M. & ELIZABETH L. HACKING

SCALE: 1"=100' JULY 30, 1976

ESSEX SURVEY SERVICE INC.
27 Federal Street Salem, Mass

In the opinion of the Boxford Planning Board,
this plan is not required to block the
public right of passage of a dead end street.

I certify that this plan was prepared in
accordance with the Rules and Regulations
of the Registers of Deeds.

This lot shall not be hereafter subdivided, reduced in
area, or changed in character so as to be subject to Section
VI, B4, subsection 2 of the Boxford Zoning By-law.

Date: 4 AUG 1976

6/30/1976 John P. Pagan
Draftsman

Approval under the Subdivision
Control Law not required.
Boxford Planning Board
Robert M. Hacking
Elizabeth L. Hacking
Green M. Hacking
John P. Pagan

Date: 4 AUG 1976

LAWRENCE
(Public Variable Width)
ROAD



Plan Register of Deeds Use Only	
PLAN BOOK 144 PLAN 35	
ESSEX REGISTRY OF DEEDS DIST.	
SALM, MASS.	
Received	Aug. 1, 1977
By: [Signature]	
Agent: John O'Brien, Jr. Register of Deeds	
paged: [blank]	