

- WESTERLY** by land shown on said plan as of Harsch, by two courses measuring, respectively, thirty-six and 58/100 (36.58) feet and one hundred forty-nine and 15/100 (149.15) feet;
- NORTHERLY** by the same, three hundred seventeen and 04/100 (317.04) feet;
- WESTERLY** by land shown on said plan as of Ward, three hundred thirty-one and 82/100 (331.82) feet;
- NORTHERLY** by the same, two hundred eighteen and 79/100 (218.79) feet;
- NORTHEASTERLY** by the same, by four courses measuring respectively, fifty-three and 24/100 (53.24) feet, seventy-one and 16/100 (71.16) feet, one hundred fifty and 97/100 (150.97) feet, and eighty-nine and 06/100 (89.06) feet;
- NORTHWESTERLY** by land shown on said plan as of Rehm, by two courses measuring, respectively, twenty-nine and 37/100 (29.37) feet and thirty-eight and no/100 (38.00) feet;
- WESTERLY** by land shown on said plan as of said Rehm, O'Brien, and Eagle Nest Hill Trust, Dorothy L. Woodbury, Trustees, by five courses measuring respectively, three hundred fourteen and 34/100 (314.34) feet, three hundred four and 71/100 (304.71) feet, three hundred thirty-five and 98/100 (335.98) feet, two hundred seventy-two and 67/100 (272.67) feet and three hundred thirty-five and 74/100 (335.74) feet;
- SOUTHERLY** by Lot 4 as shown on said plan, twenty-four and 86/100 (24.86) feet; and
- WESTERLY** by the same and by land shown on said plan as of Estate of William J. Greenler, Jr., by two courses measuring, respectively, three hundred fifty-one and 94/100 (351.94) feet and two hundred twelve and 66/100 (212.66) feet;

Containing thirty-five and 27/100 (35.27) acres, more or less, according to said plan.

Being a portion of the premises conveyed to the Grantor by Charles B. Abbott, Trustee, by deed dated April 20, 1988, recorded with said Registry of Deeds Book 9553, Page 156.

BK010283-038

Shaven
Crown B


EXHIBIT B

original on file at Greenbelt
office.

Driveway on
BTA/BOLT
Land.



ASSESSOR'S MAP 10-1-75

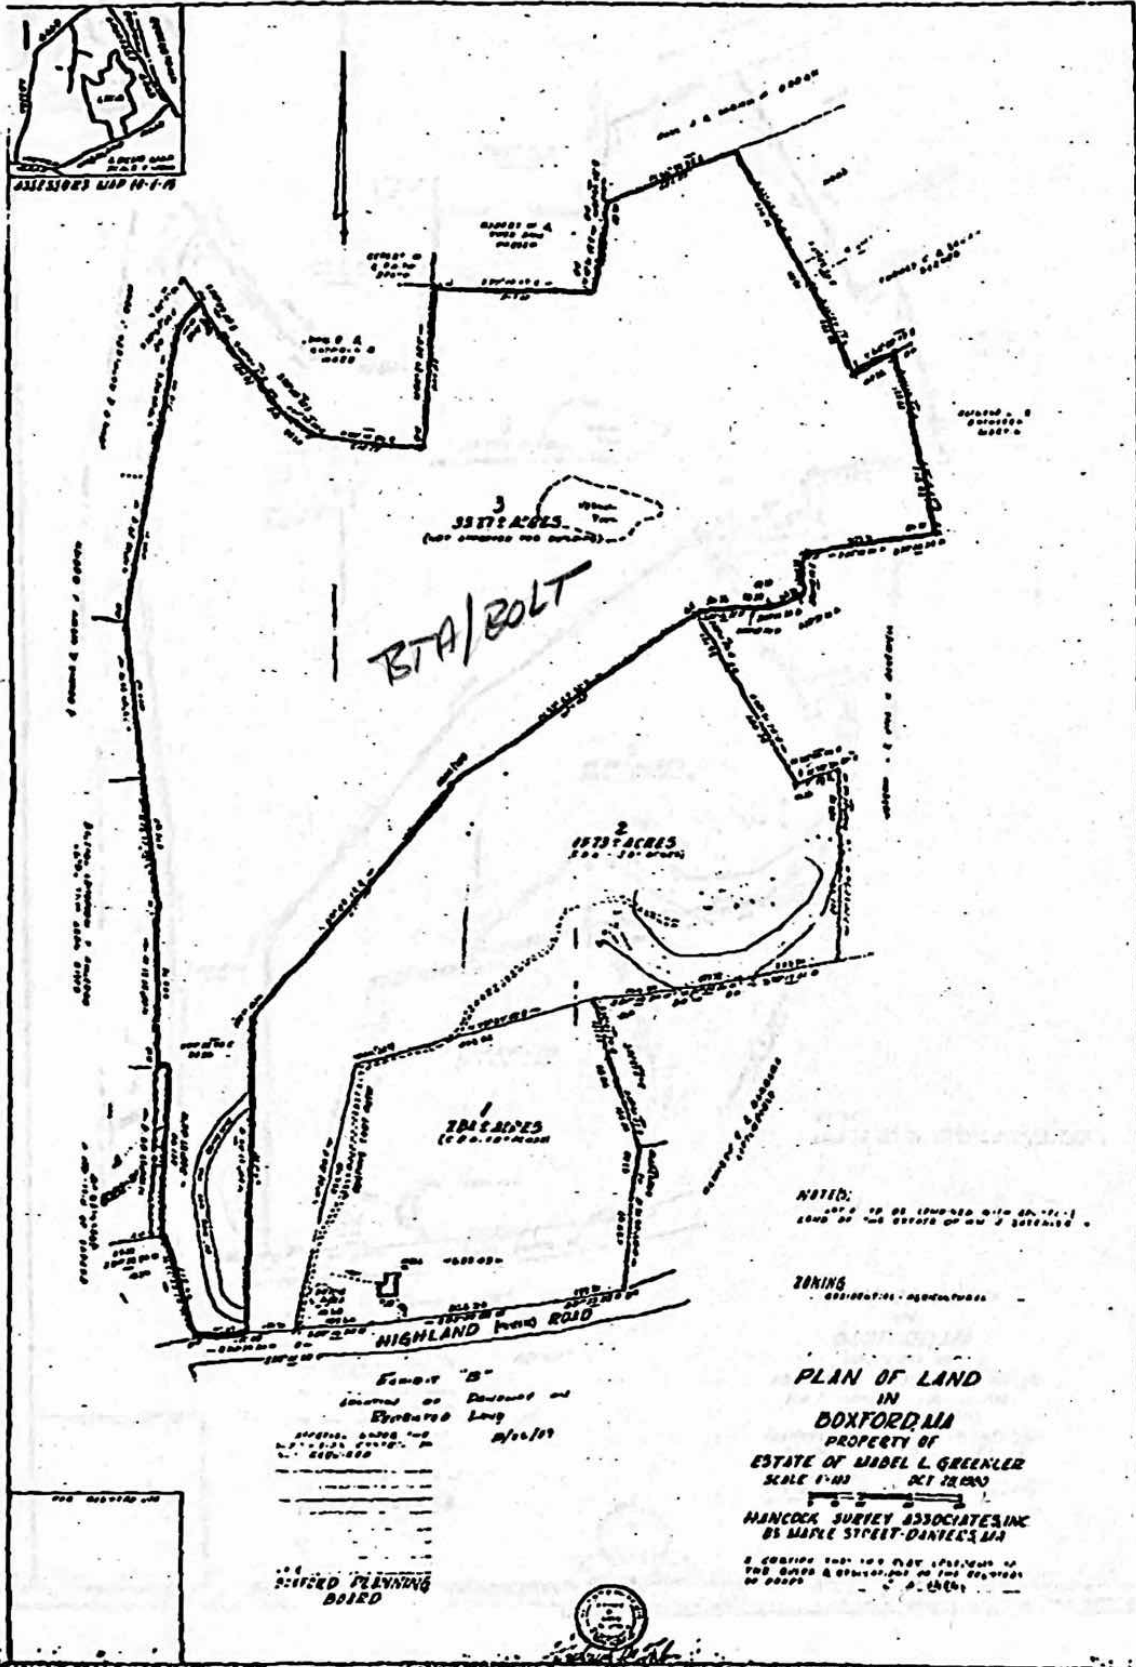

NOTED:
LOT 2 IS BE LEASED WITH AN 11-1
LAND OF THE ESTATE OF MR. J. DANIELS

ZONING
RESIDENTIAL - AGRICULTURAL

PLAN OF LAND
IN
DOXFORD, MA
PROPERTY OF
ESTATE OF MABEL L. GREENLER
SCALE 1"=1/2 MI OCT 1960

HANCOCK SURVEY ASSOCIATES INC
85 MAPLE STREET-DANVERS, MA

2. CONTAIN THE 100 FOOT WIDE STRIP OF
THE ROAD & STRIP OF LAND TO THE RIGHT
OF ROAD

EXHIBIT "B"
Location of Roadway and
Easement Map
APPROVED UNDER THE
MASSACHUSETTS
GENERAL LAWS
8/16/60


MASSACHUSETTS
PLANNING
BOARD



EXHIBIT B

original on file at Greenbelt
office.

Driveway on
BTA/BOLT
land.

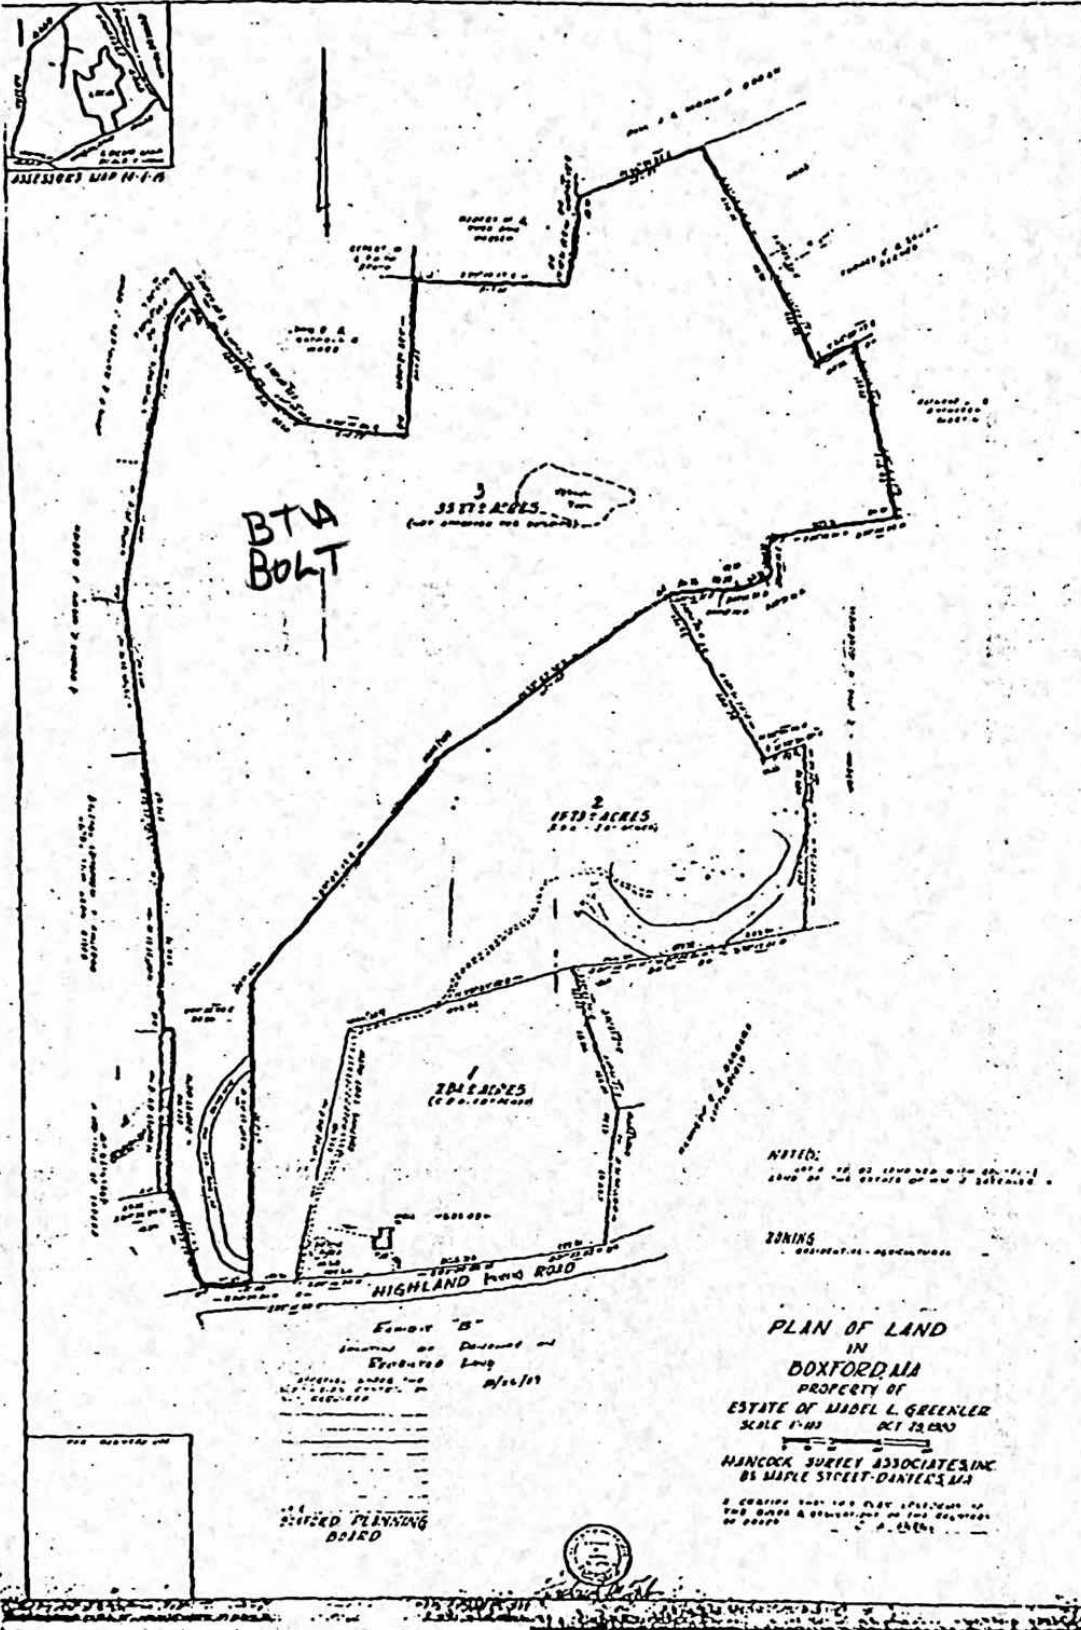

REFERENCES:

DEED - BK. 14087 PG. 12
 PLAN - PL. BK. 182 PL. 48

LEGEND & SYMBOLS

STONE WALL
 D.H. DRILL HOLE
 U.L. UPRIGHT IRON ROD
 P.L. FOUND


MARKING OF LOT LINES

FOR

BTA/BOLT, INCORPORATED
 BOXFORD, MA

SCALE: 1" = 40'
 MAY 8, 2001
 DONOHUE AND PARKHURST, INC.
 383 BOSTON ST.,
 TOPSFIELD, MA
 (978) 887-8181

SCALE:
 0 20 40 60 80 100 120 140
 FEET
 0 10 20 30 40
 METERS

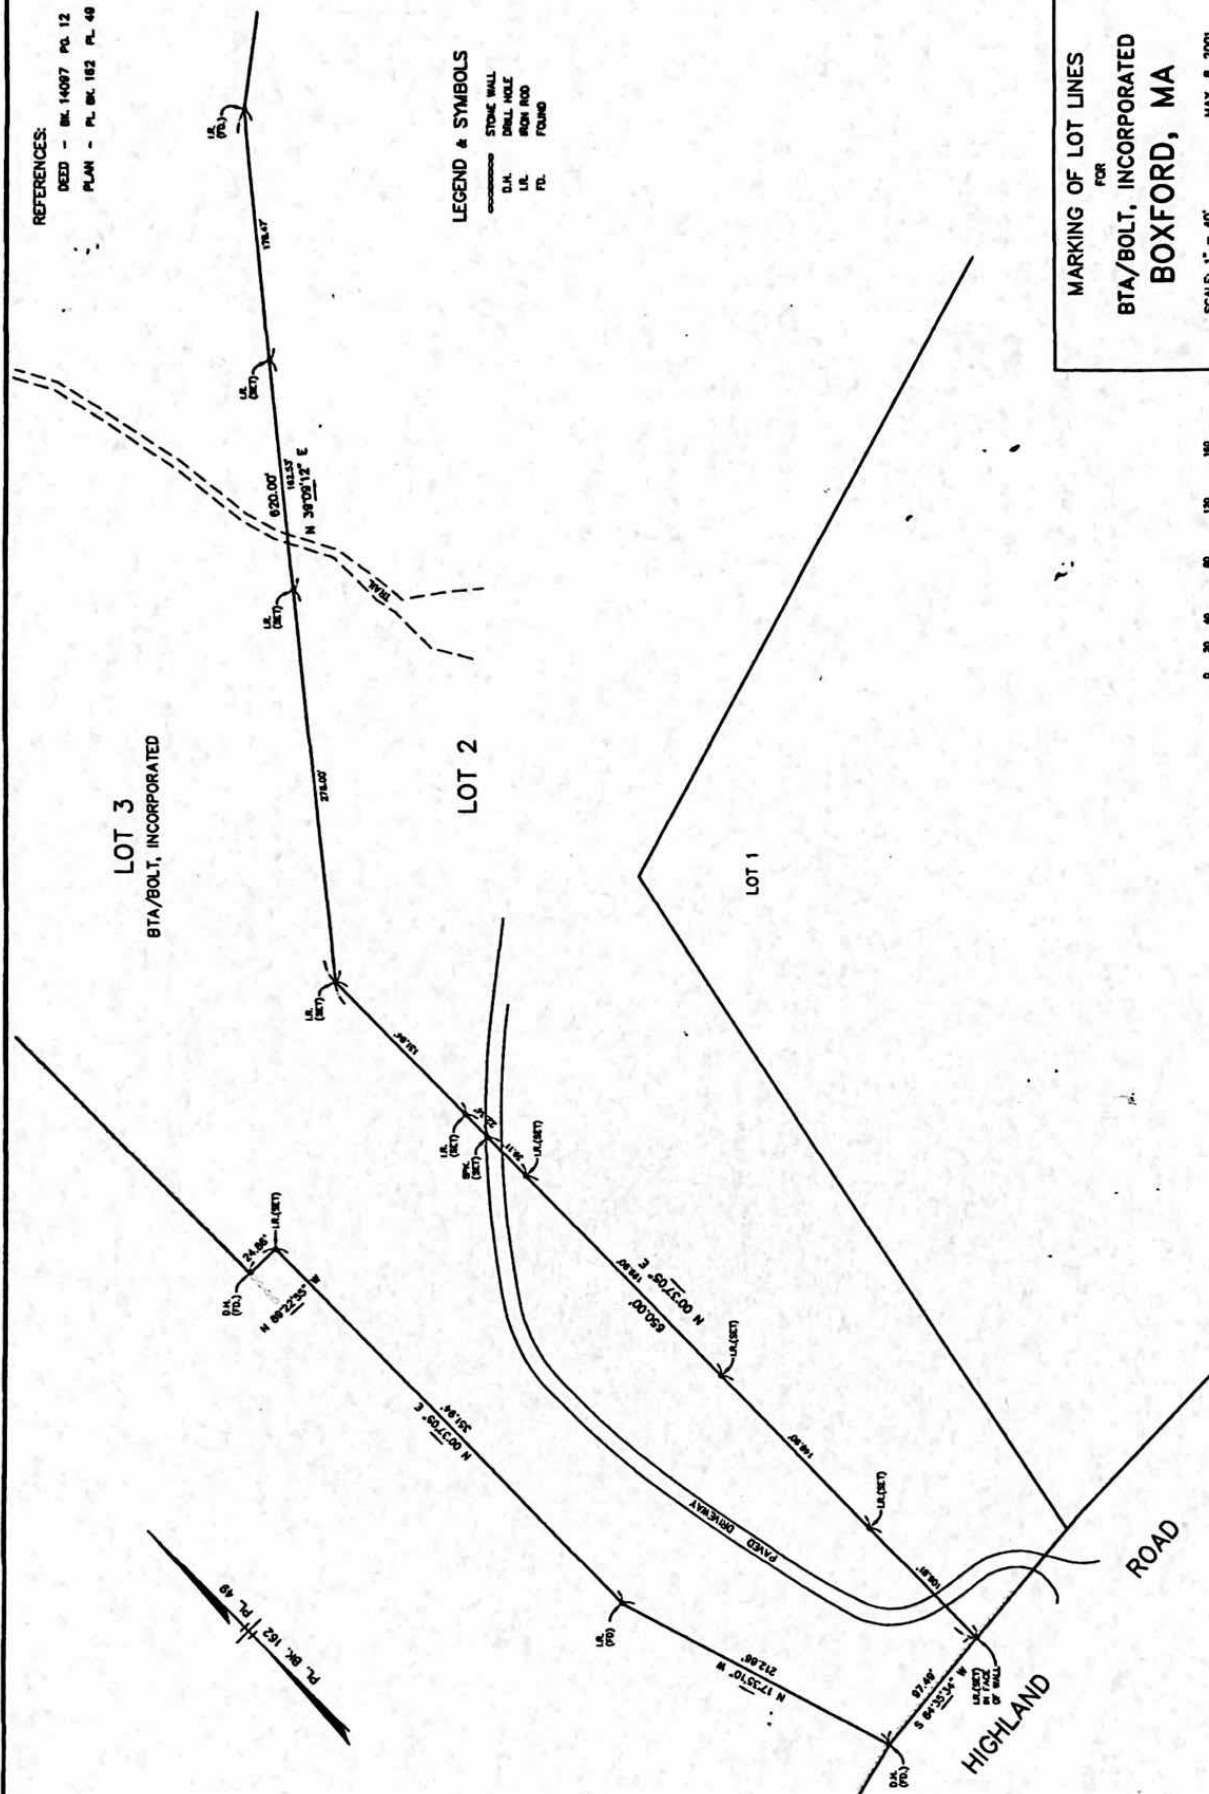

BOX-F Hoslinger Conservation Restriction



Legend

-  Greenbelt Fee Properties
-  Greenbelt CRs

0 0.25 0.5 1
Miles

USGS quadrangles provided by MassGIS.
1:25,000.

Boundaries are approximate, and based
primarily on assessor's data.

Map produced by Essex County Greenbelt.
March 2007



BOX-F Hoslinger Conservation Restriction



0 50 100 200 Feet



Greenbelt CRs



Greenbelt Fee Properties




Color orthophotos provided by MassGIS.
1:5,000. Photos taken April 2001.

Boundaries are approximate, and based
primarily on assessor's data.

Map produced by Essex County Greenbelt.
March 2007



234942

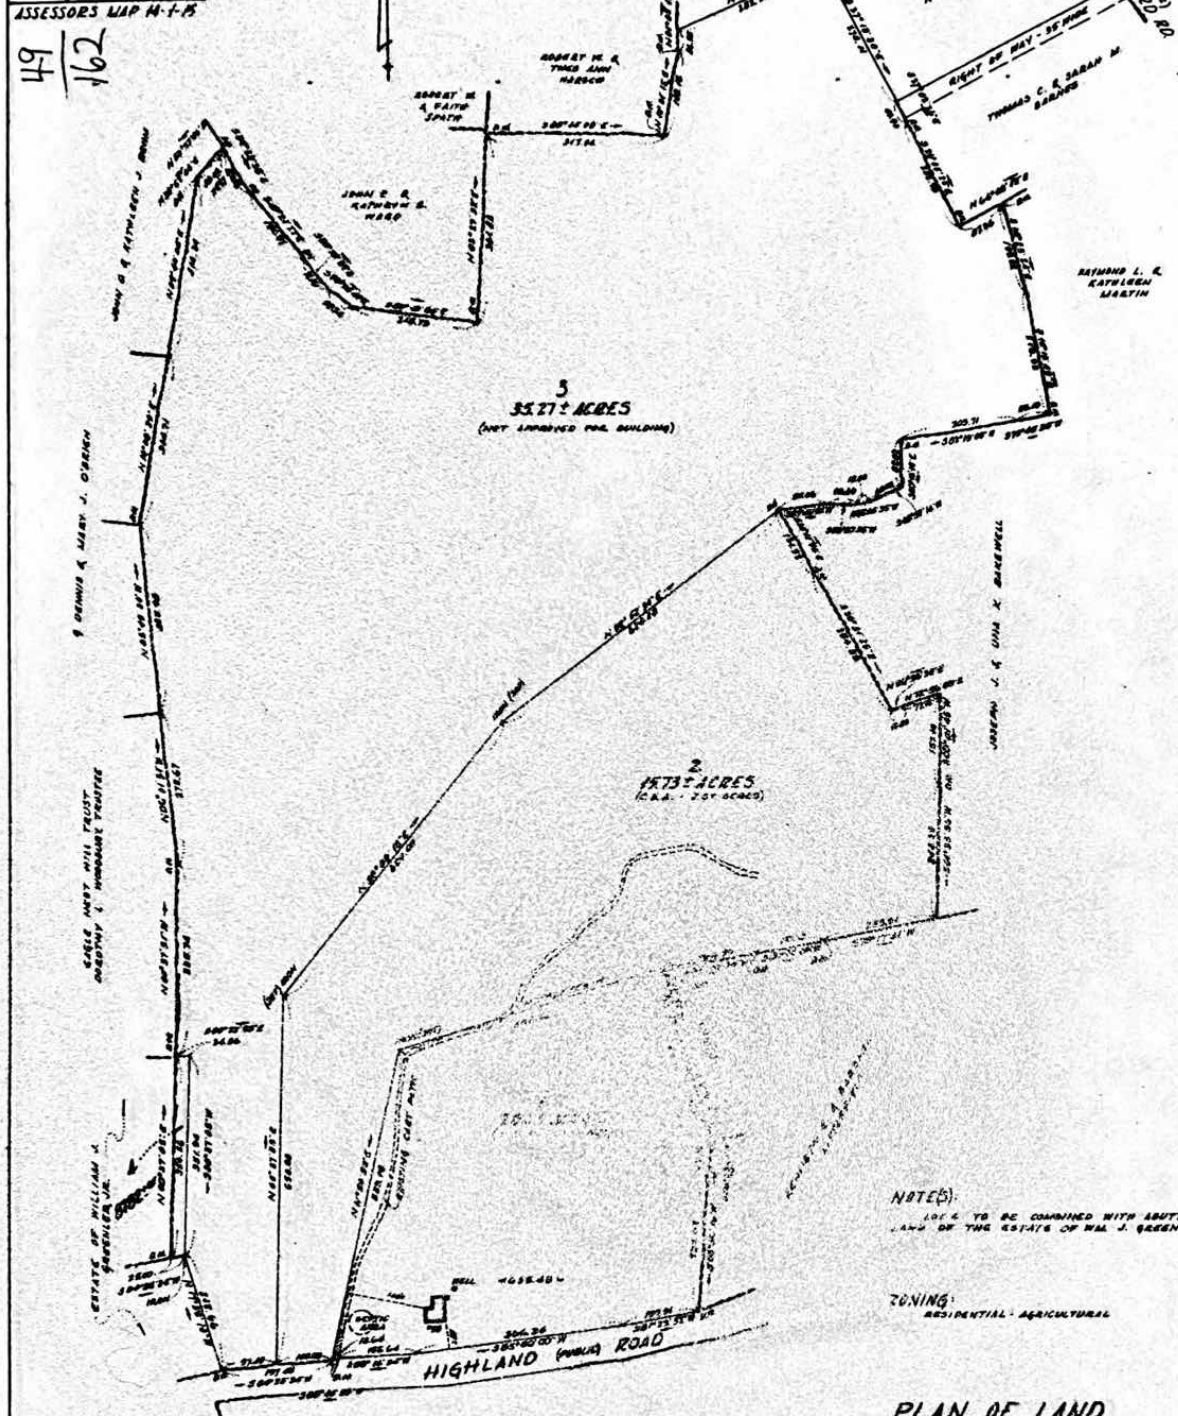

For easement

Day Map #14

