


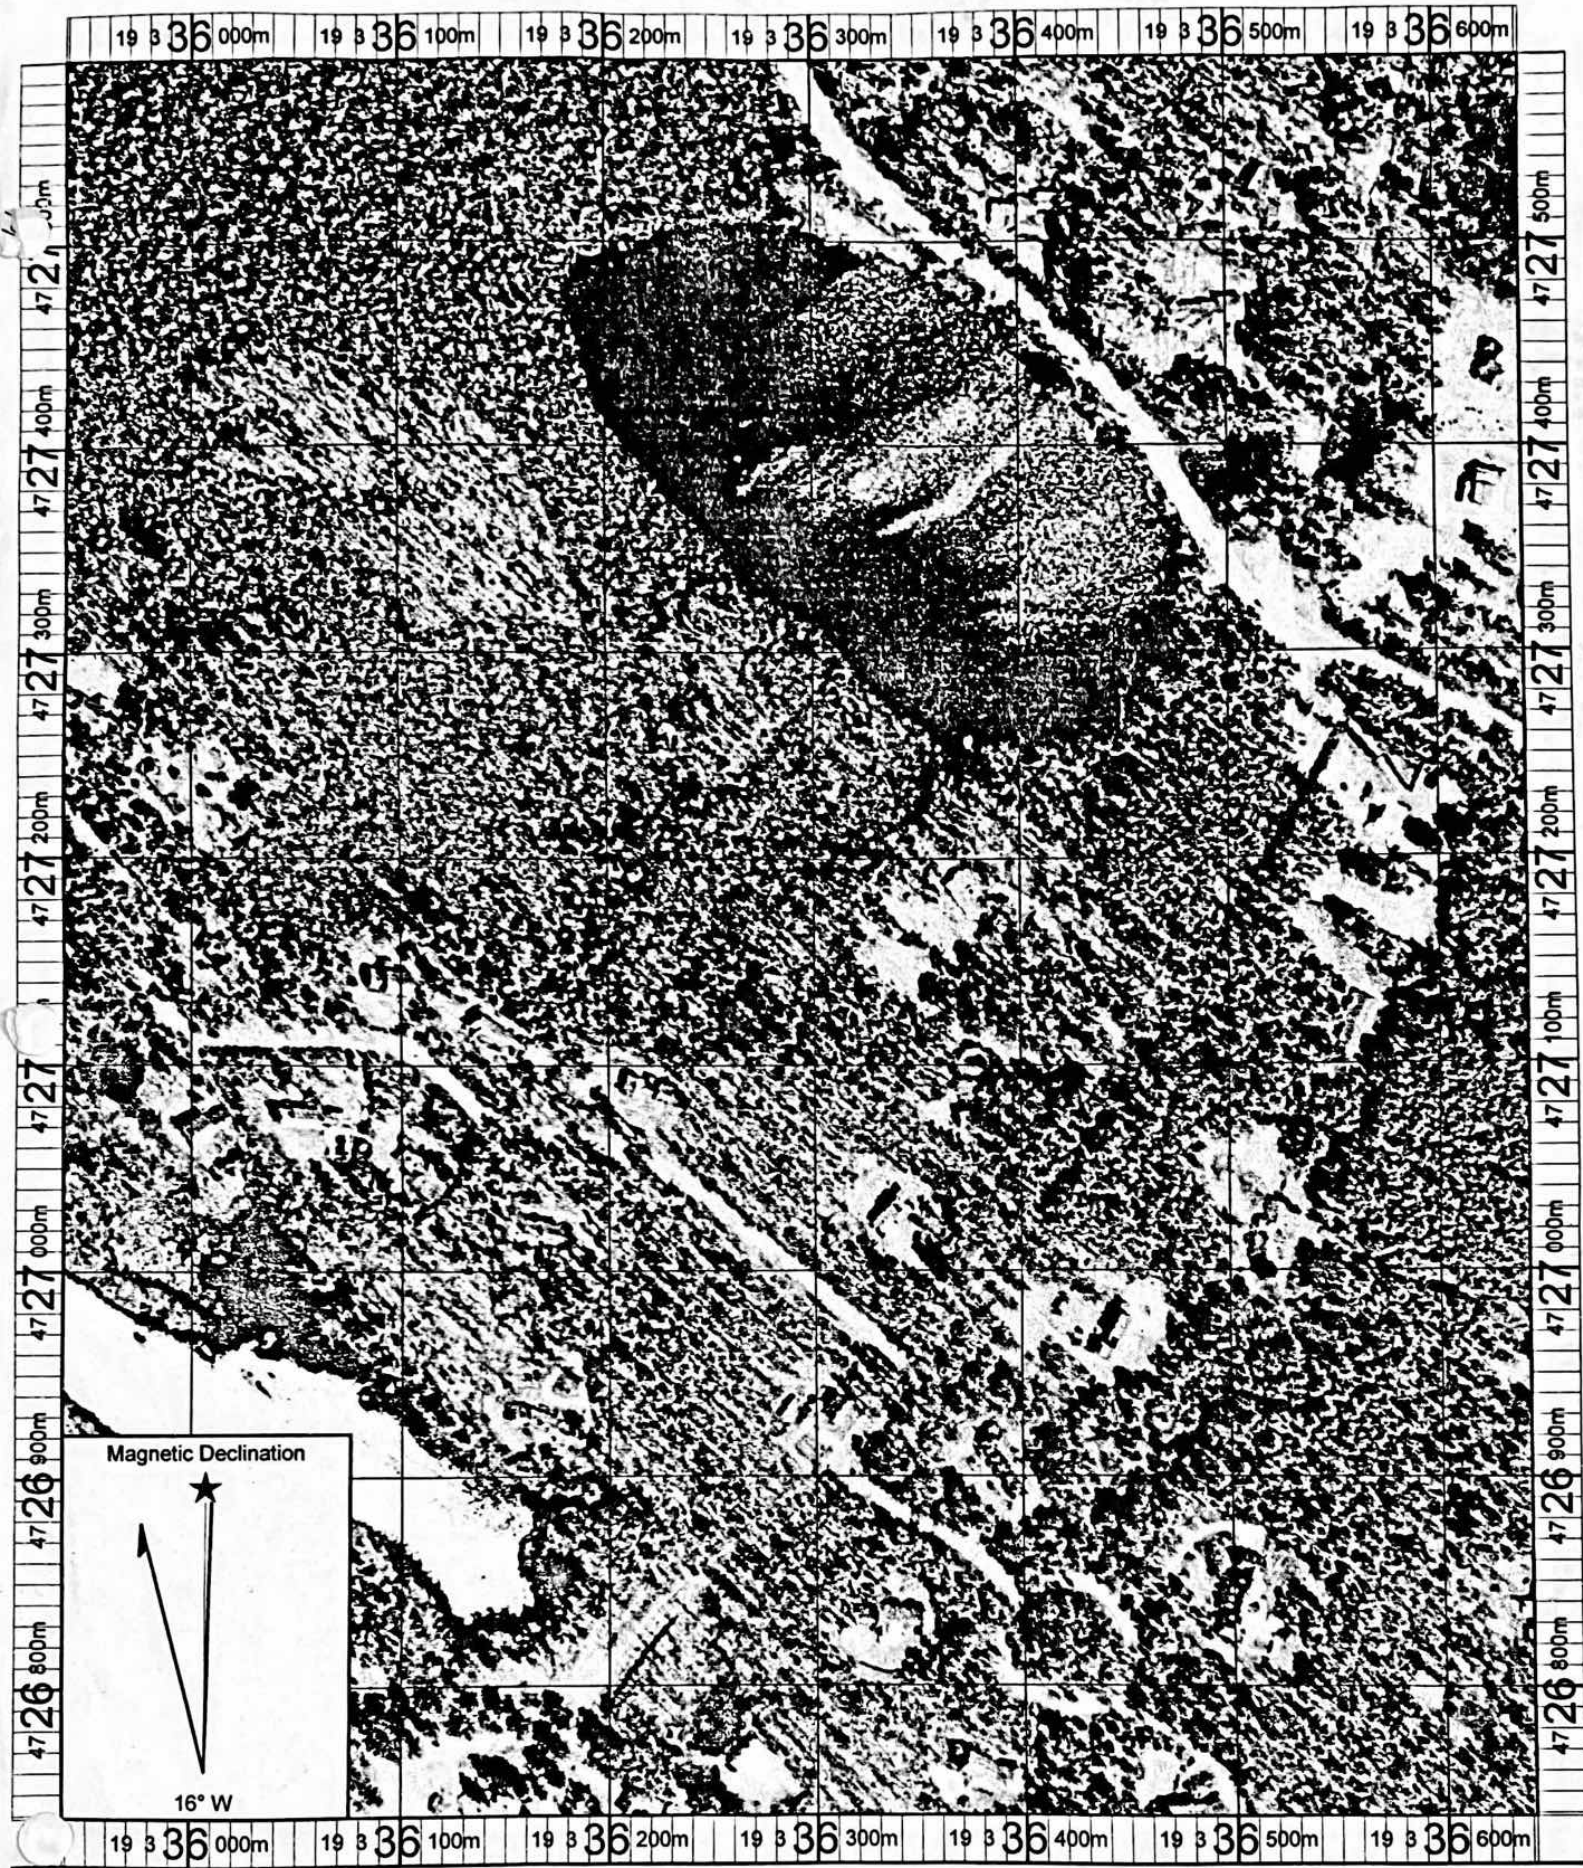


Name: GEORGETOWN SW NW, MA
Date: 8/15/2008
Scale: 1 inch equals 300 feet

Location: 19 0336288 E 4727165 N NAD 27
Caption: Stevens Pond
1:7200A; 200%

IPSWICH ROAD 1973 CO. LAYOUT

IPSWICH ROAD

50' WDE - 1973 CO. LAYOUT

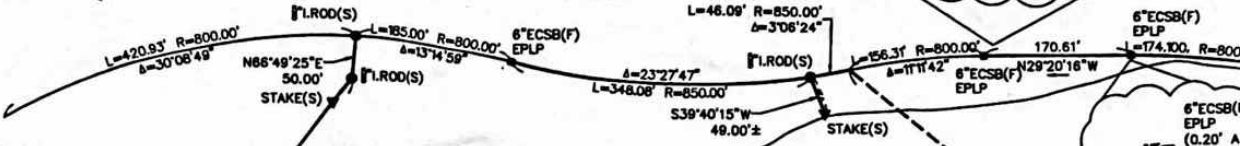

ARVIND K. AND
NILA A. PANCHOLI
BOOK 11646 PAGE 247
PLAN 28 OF 1983

CHARLES AND MARIA
E. APOSTOLOPOULOS
BOOK 18049 PAGE 240
PLAN 176 OF 1981

BOXFORD FRIENDSHIP
FOUNDATION, INC.
BOOK 7680 PAGE 504
PLAN BOOK 195, PLAN 20

GREGG AND JANE B. SPIRO
BOOK 24978 PAGE 113
PLAN BOOK 158, PLAN 87

ANTHONY V. AND
GERIANNE M. CARUSO
BOOK 14708 PAGE 354
PLAN BOOK 158, PLAN 87

ROBERT C. AND
FAITH L. BARRINGER
BOOK 26602 PAGE 227
PLAN BOOK 158, PLAN 87


PETER K. OSBORN AND
CHRISTINE M. CHADWICK
BOOK 29329 PAGE 212
PLAN BOOK 158, PLAN 87


TARBOX FAMILY
REALTY TRUST
BOOK 13960 PAGE 1
PLAN BOOK 158, PLAN 87

BTA/BOLT
BOOK 15315 PAGE 41
PLAN BOOK 212, PLAN 47

STEVENS POND

1560 +/-
BY STEVENS POND

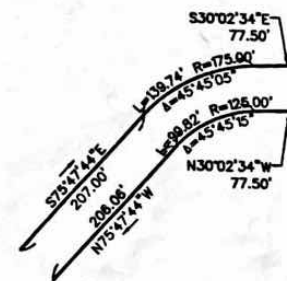

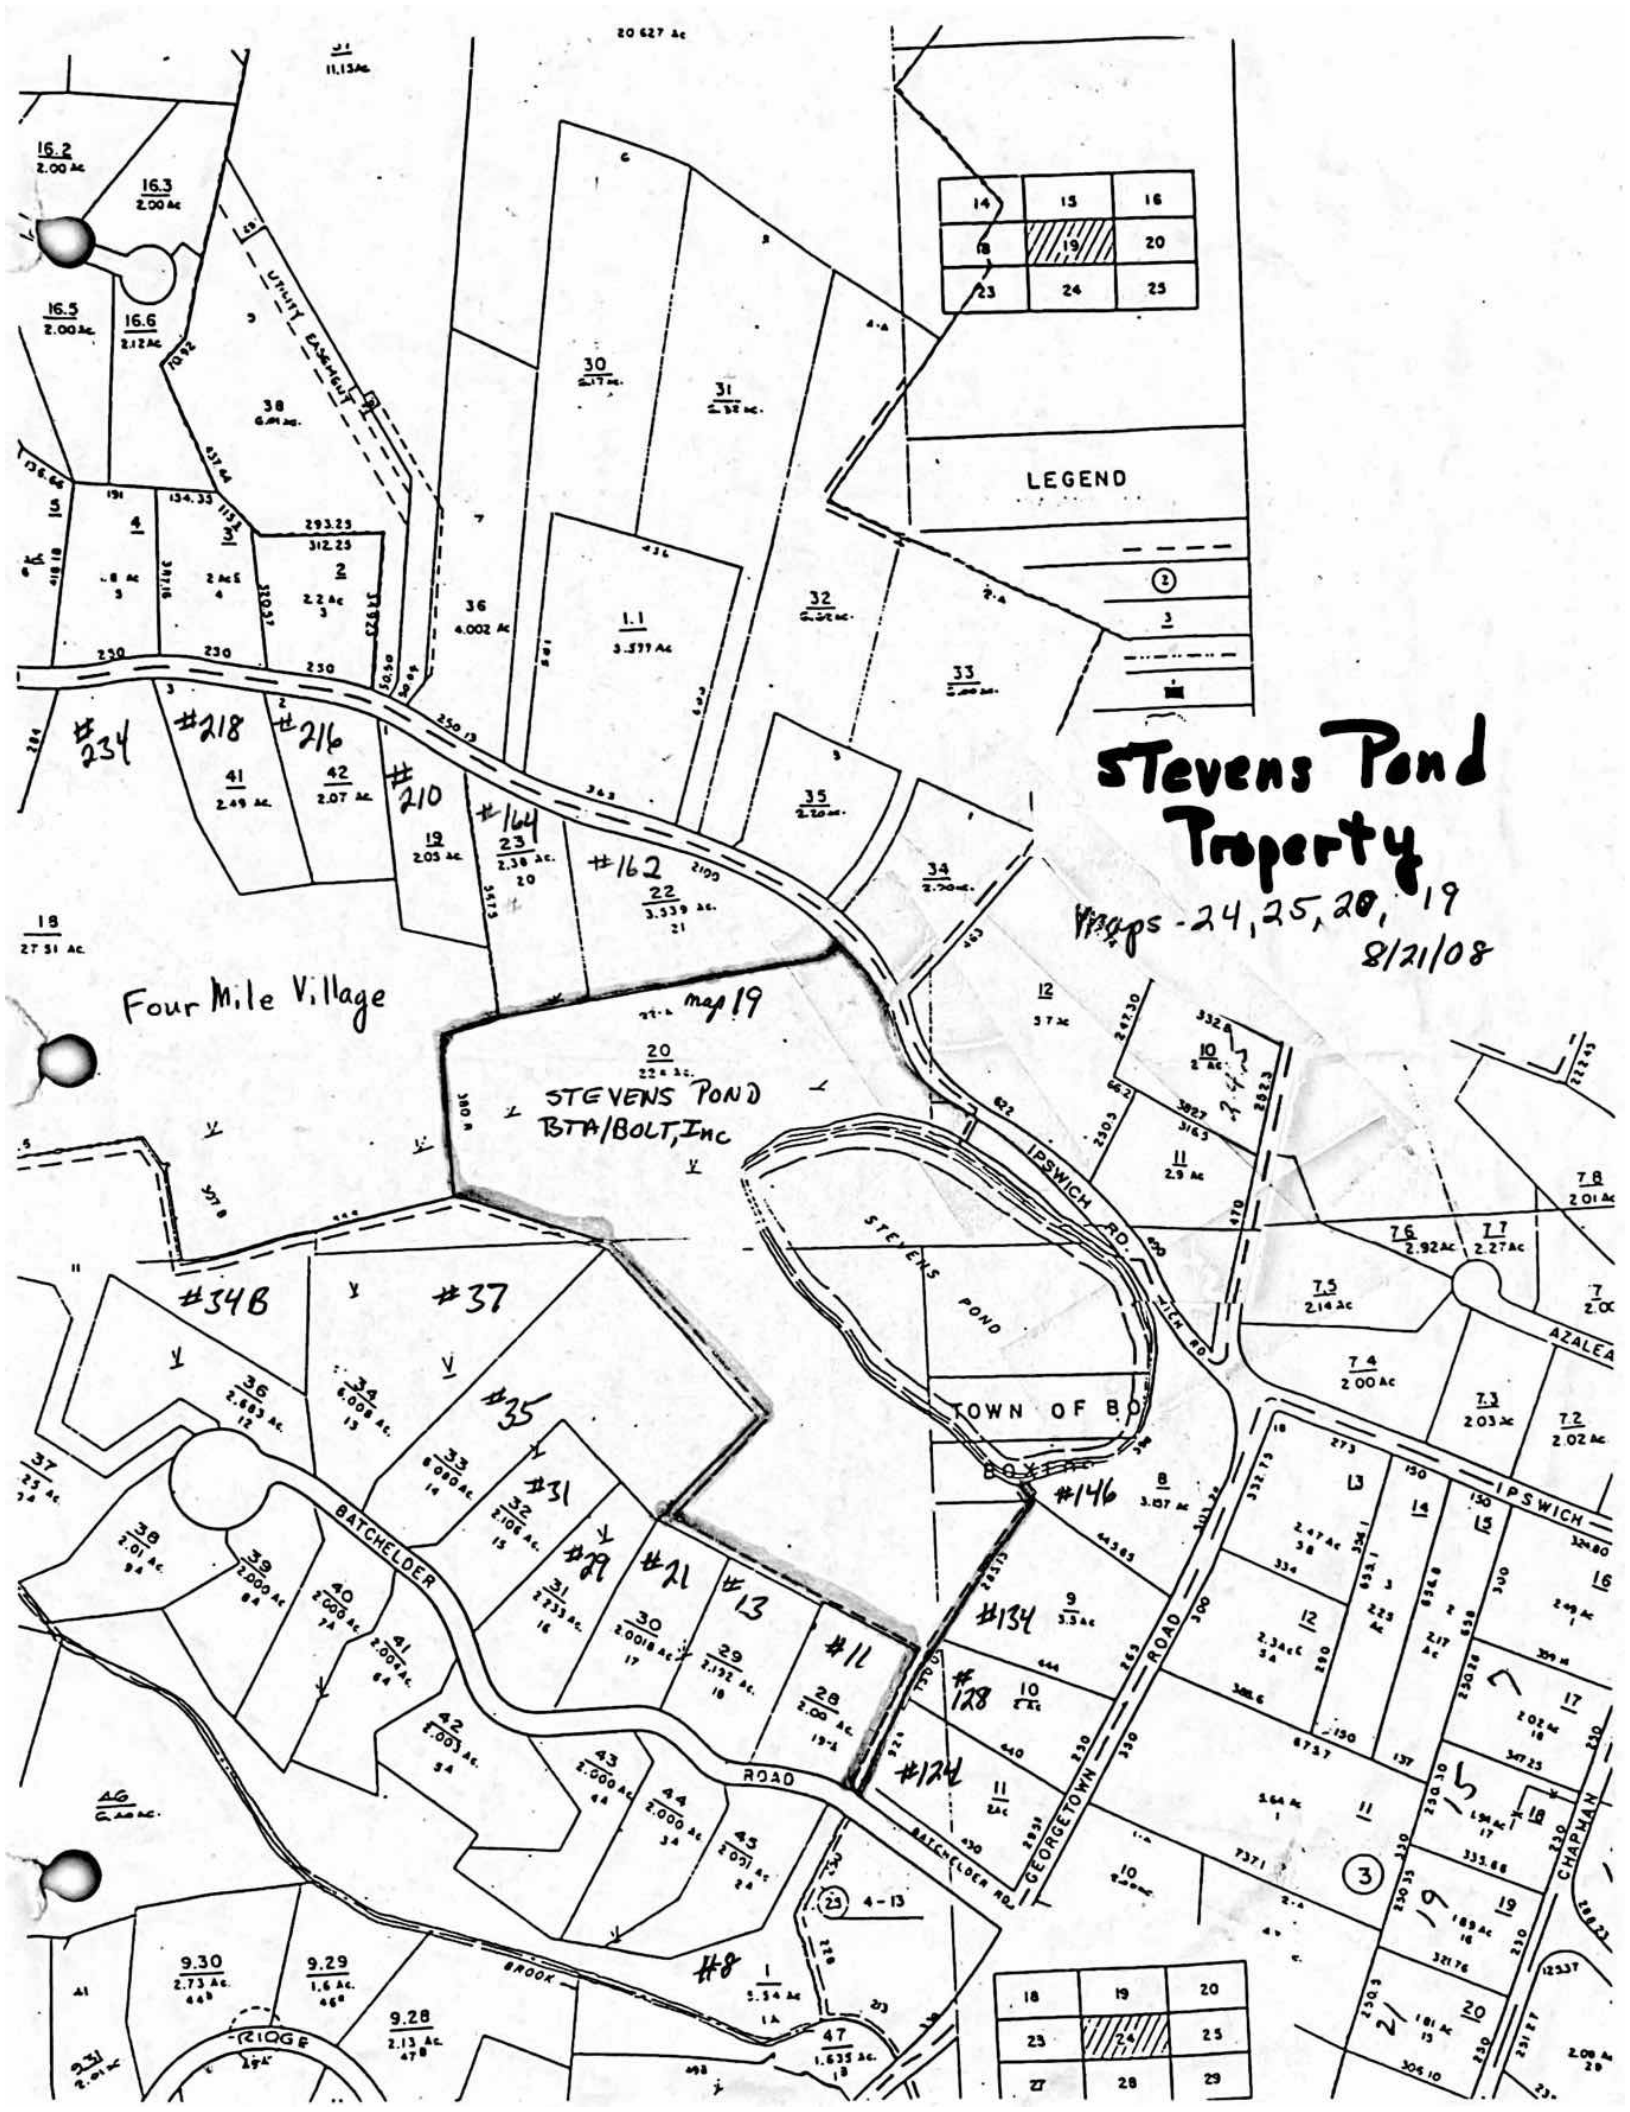

14	15	16
18	19	20
23	24	25

LEGEND

Stevens Pond Property

Maps - 24, 25, 20, 19
8/21/08

STEVENS POND
BTA/BOLT, INC

Four Mile Village

TOWN OF B

18	19	20
23	24	25
27	28	29